Tento dokument je výhradným vlastníctvom spoločnosti Energovision s.r.o.
a nesmie byť zobrazovaný alebo kopírovaný žiadnej tretej strane v súlade
s medzinárodným zákonom o autorských právach.

© Všetky práva vyhradené

energovision

Moderné energetické riešenia, ktoré hľadáte

Energovision s.r.o.

Lamačská cesta 1738/111
Bratislava 841 03
Slovenská republika

info@energovision.sk
www.energovision.sk

Zákazník		
Projekt		
Stupeň projektu		
Označenie dokumentu		
Číslo zákazky		
Sieť AC		TN-S
Sieť DC		IT
Silové napätie AC		3+N+PE 400/230V~50Hz
Silové napätie DC		2x 1000V DC
Ovládacie napätie		1+N+PE 230V~50Hz
Ochrana proti dotyku na neživú časť do 1000V/AC a 1500V/DC	Základná	Ochrana samočinným odpojením napájania
	Doplnková	Doplnkové pospojovanie

Dátum: Vypracoval: Kontroloval: Schválil:

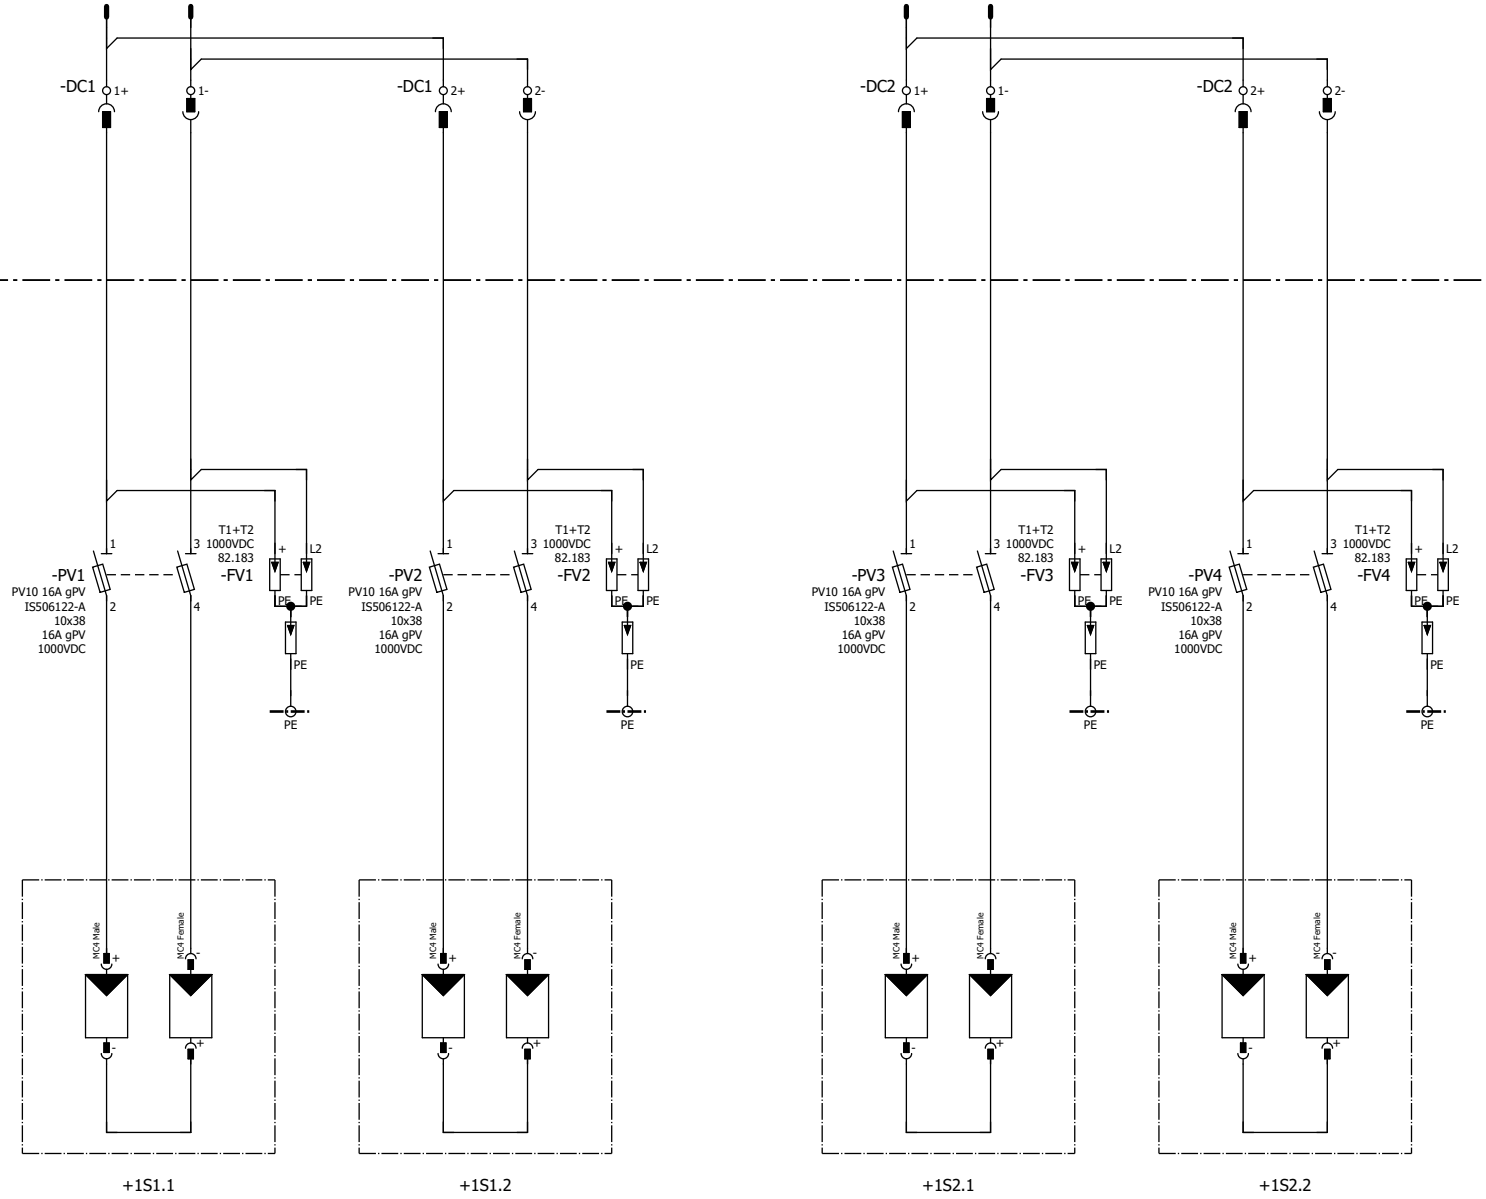

1

3

Stupeň:	energovision Moderné energetické riešenia, ktoré hľadáte	Dátum		Projekt		Číslo zákazky	= FVZ
Revízia: 1		Vypracoval		Zákazník			
Meno:		Kontroloval		Miesto stavby		Označenie dokumentu	Strana 2
Dátum:		*Energovision s.r.o.*			Wiring diagram		Strán 5

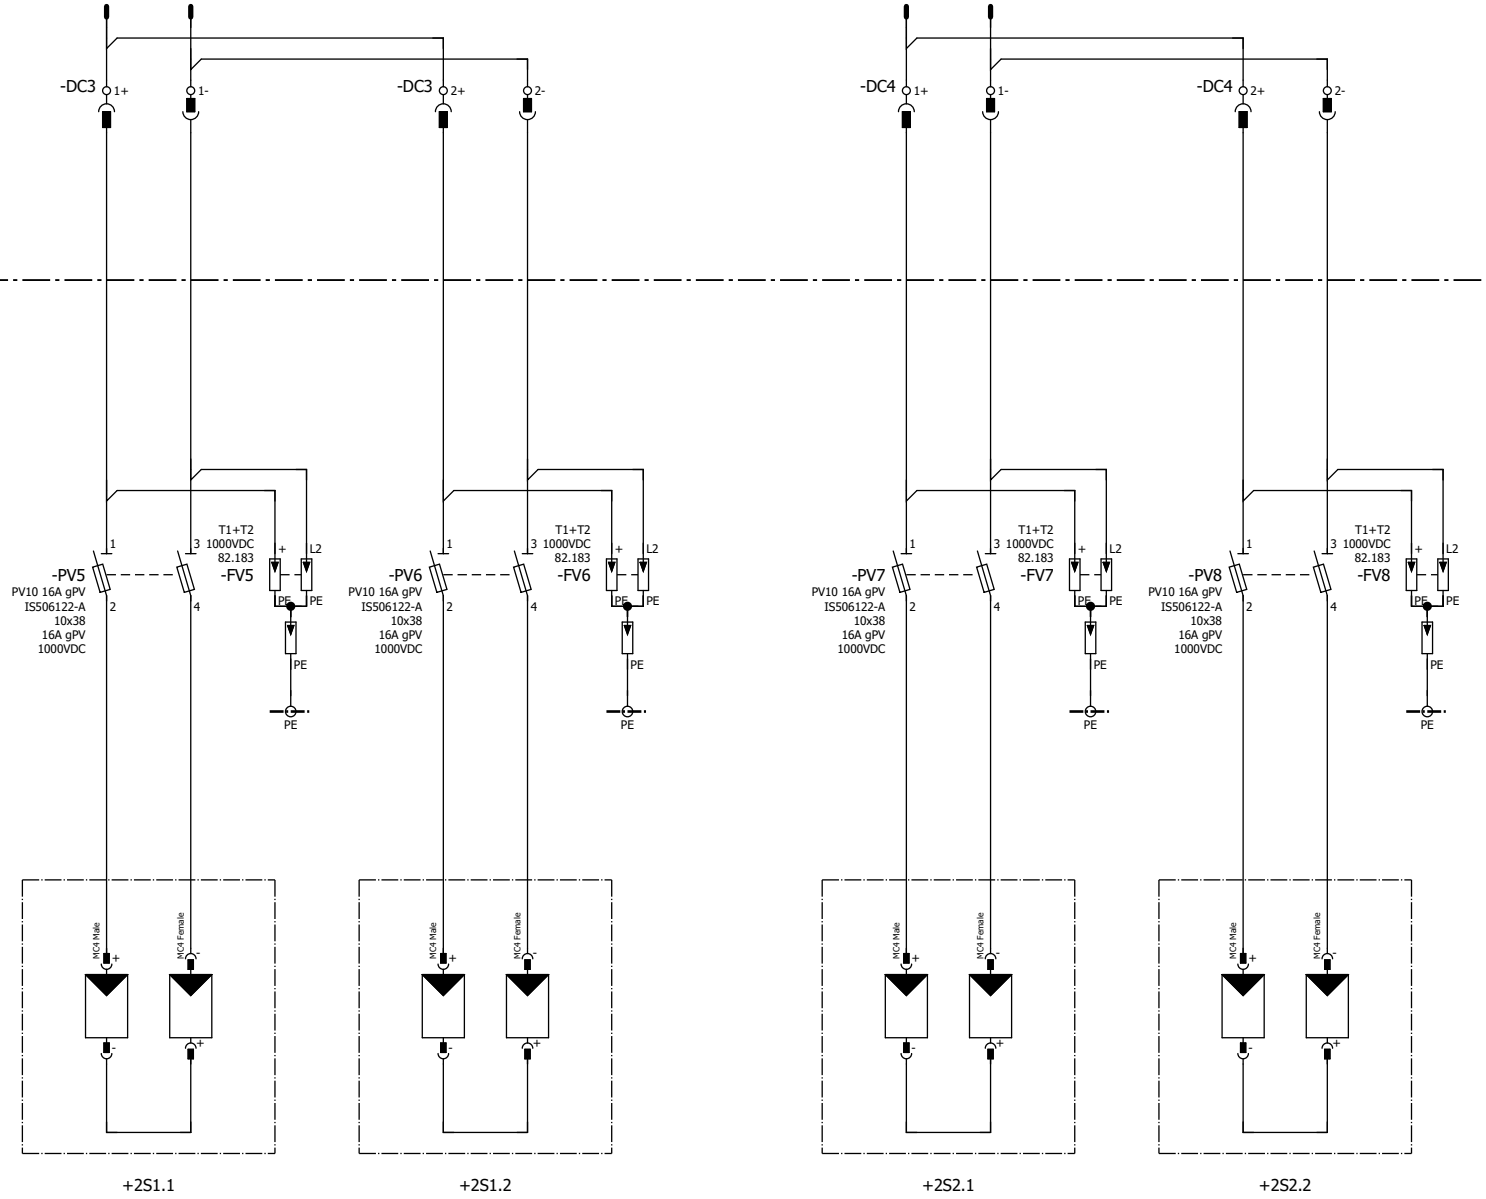

2

4

Stupeň:	energovision Moderné energetické riešenia, ktoré hľadáte	Dátum		Projekt		Číslo zákazky	= FVZ
Revízia: 1		Vypracoval		Zákazník			
Meno:		Kontroloval		Miesto stavby		Označenie dokumentu	Strana 3
Dátum:		*Energovision s.r.o.*			Wiring diagram		Strán 5

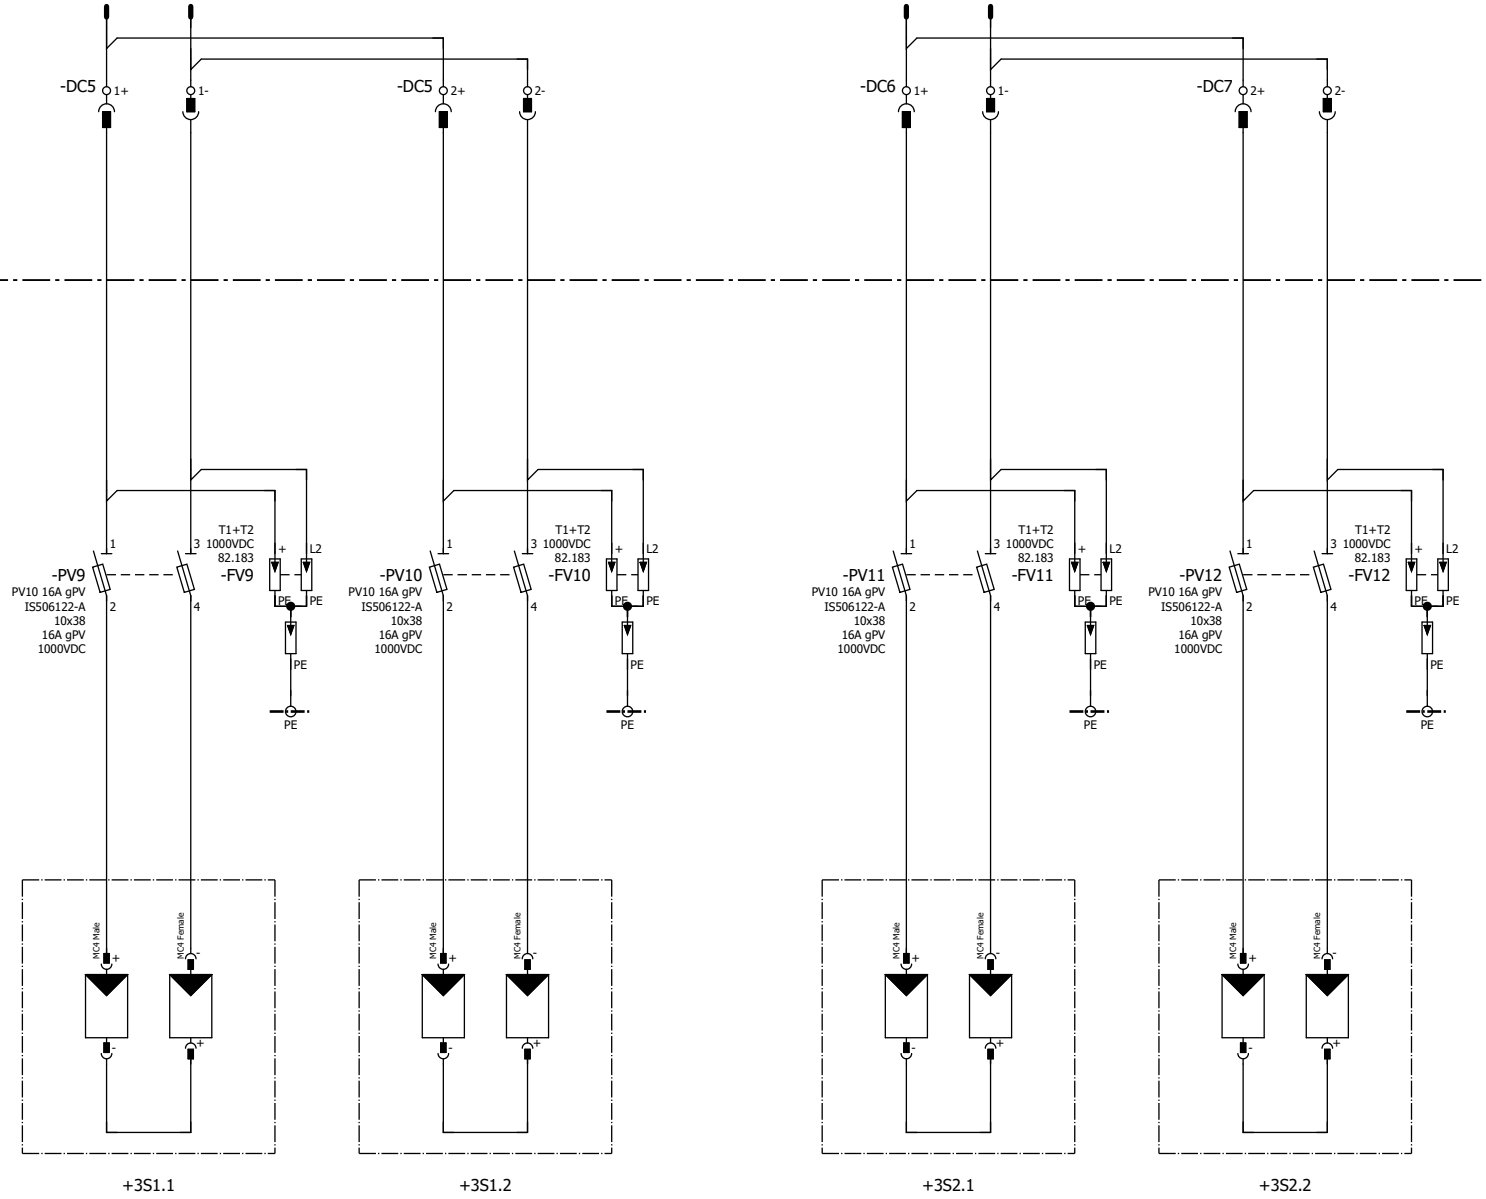

3

5

Stupeň:	energovision Moderné energetické riešenia, ktoré hľadáte	Dátum		Projekt		Číslo zákazky	= FVZ
Revízia: 1		Vypracoval		Zákazník			
Meno:		Kontroloval		Miesto stavby		Označenie dokumentu	Strana 4
Dátum:		*Energovision s.r.o.*			Wiring diagram		Strán 5

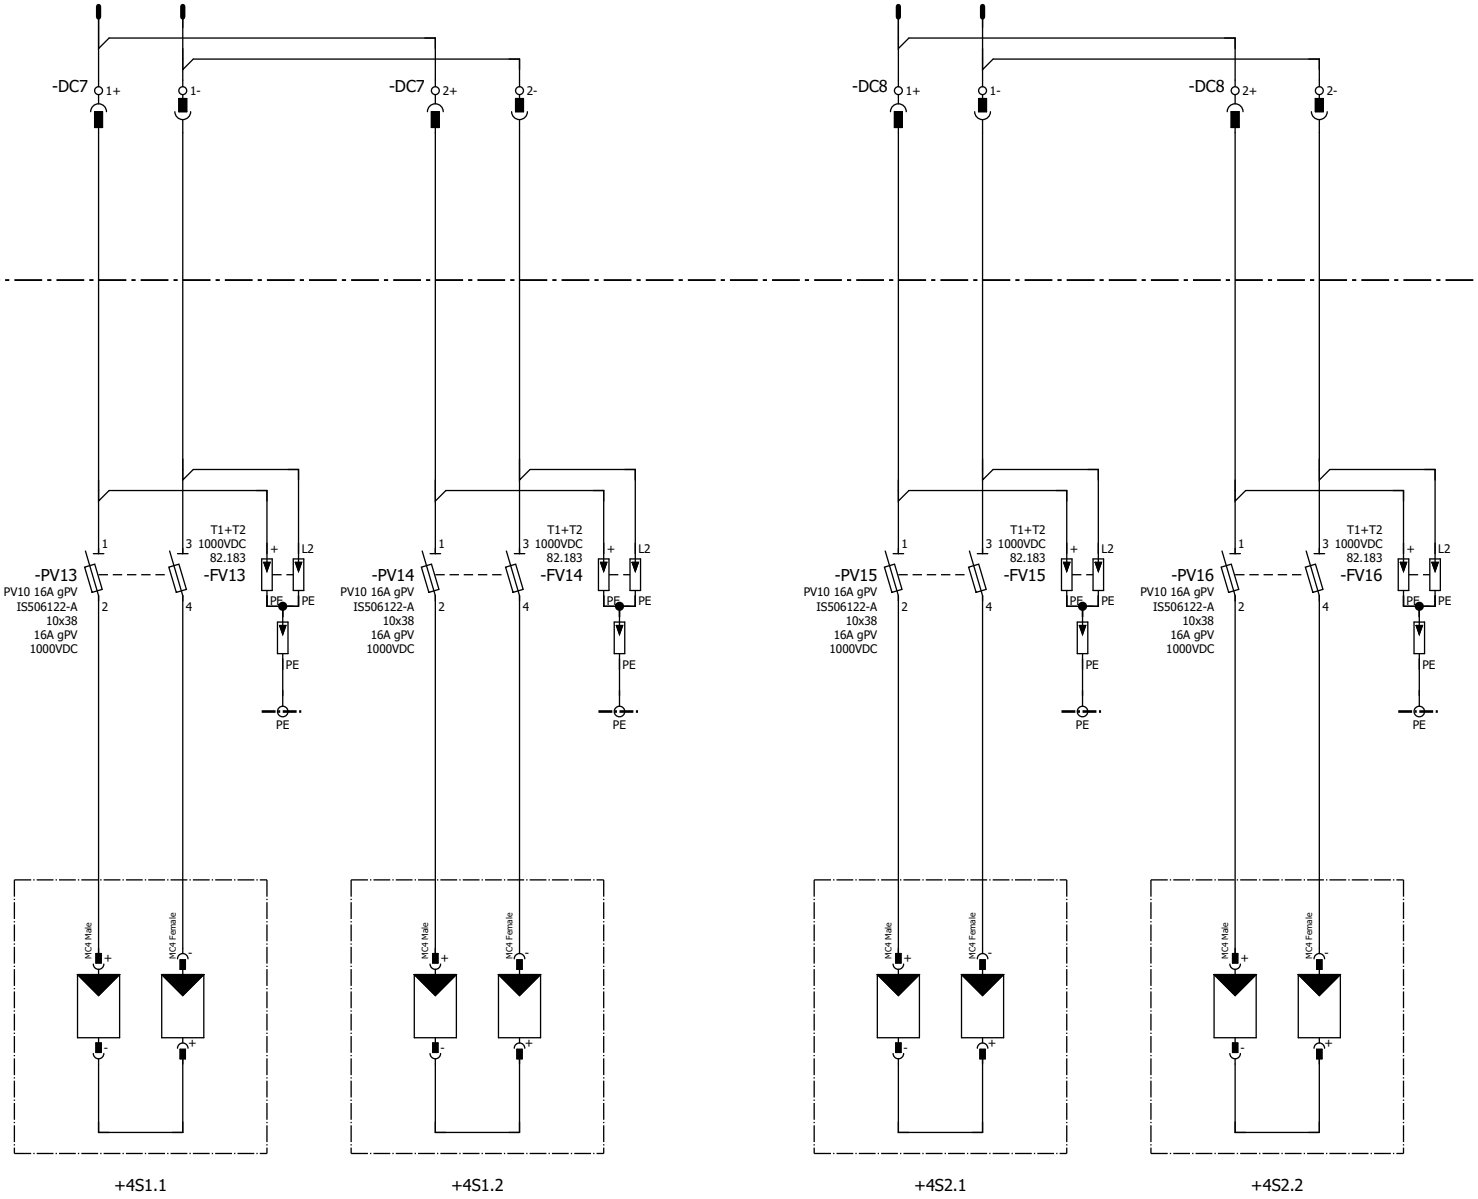

4

6

Stupeň:	energovision Moderné energetické riešenia, ktoré hľadáte	Dátum		Projekt		Číslo zákazky	= FVZ
Revízia: 1		Vypracoval		Zákazník			
Meno:		Kontroloval		Miesto stavby		Označenie dokumentu	Strana 5
Dátum:		*Energovision s.r.o.*			Wiring diagram		Strán 5